

STATE OF UTAH DEPARTMENT OF NATURAL RESOURCES DIVISION OF OIL, GAS AND MINING										FORM 8	
WELL COMPLETION OR RECOMPLETION REPORT AND LOG										1. WELL NAME Brutus Buckeye 26-13-8-16-3H	
2. TYPE OF WELL Oil Well			3. TYPE OF WORK DRILL NEW ☒ REENTER P&A ☐ DEEPEN ☐ RECOMP ☐							4. API NUMBER 4301354612	
5. NAME OF OPERATOR Scout Energy Management, LLC					6. OPERATOR PHONE 972-325-1027			7. FIELD NAME MONUMENT BUTTE			
8. ADDRESS OF OPERATOR 13800 Montfort Drive, Suite 100, Dallas, TX, 75240					9. OPERATOR E-MAIL tbrown@scoutep.com			10. UNIT NAME Greater Monument Butte			
11. MINERAL LEASE NUMBER MULTIPLE LEASES			12. MINERAL OWNERSHIP FEDERAL			13. SURFACE OWNERSHIP FEDERAL			14. COUNTY DUCHESNE		
15. DATE SPUDDED (SPUD RIG) 01/05/2024		16. DATE SPUDDED (ROTARY RIG) 01/21/2024		17. DATE TOTAL DEPTH REACHED 02/23/2024		18. DATE COMPLETED/ABANDONED 07/26/2024			19. DATE OF FIRST PROD. / INJ. PROD:08/01/2024 INJ:		
20. DEPTH REFERENCE GROUND LEVEL ☒ KELLY BUSHING ☐ DERRICK FLOOR ☐					21. DEPTH REFERENCE ELEVATION 5571 (US Feet)			22. GRADED GROUND LEVEL ELEVATION 5571 (US Feet)			
23. WELLBORE DEVIATION PROFILE VERTICAL ☐ DIRECTIONAL ☐ HORIZONTAL ☒					24. TOTAL DEPTH MD 17405 TVD 6893			25. PLUGGED BACK TOTAL DEPTH MD TVD			
26. CURRENT WELL STATUS Producing											

27. LOCATION OF WELL									
WELL POSITION	FOOTAGES		QTR-QTR	SECTION	TOWNSHIP	RANGE	MERIDIAN	UTM EASTING	UTM NORTHING
Surface	1882 FSL	1365 FEL	NWSE	26	8.0 S	16.0 E	S	578254	4437797
Producing Interval Top	936 FSL	1183 FEL	SWSE	26	8.0 S	16.0 E	S		
Producing Interval Bottom	509 FNL	2223 FWL	LOT3	13	8.0 S	16.0 E	S		
Total Depth	498 FNL	2227 FWL	LOT3	13	8.0 S	16.0 E	S		

28. HOLE, CASING AND CEMENT INFORMATION																
STRING	HOLE SIZE	CASING O.D.	WEIGHT	GRADE	THREAD	TOP (MD)	BOTTOM (MD)	DV TOOL DEPTH	LEAD TAIL	CEMENT TYPE	SACKS	YIELD	WEIGHT	CEMENT TOP	BASIS FOR TOP	
COND	24.0	16.0	65.0			0	108			Class G Cement	100	1.17	15.8	0	Circulate	
SURF	12.25	9.625	36.0	J-55	BTC	0	1532		L	Class G Cement	330	1.77	13.1	0	Circulate	
									T	Class G Cement	250	1.16	15.8			
PROD	8.75	5.5	20.0	P-110	BTC	0	6319		L	Class G Cement	650	2.92	11.5	0	Circulate	
P2	7.875	5.5	20.0	P-110	BTC	6319	17390		T	Class G Cement	1970	1.43	14.0			

29. TUBING RECORD			
TUBING SIZE	TOP (MD)	BOT (MD)	PACKER DEPTH
2.725	0	6250	6231

30. RETRIEVABLE / TEMPORARY PLUGS		
PLUG	DEPTH (MD)	TYPE

31. PERMANENT / ABANDONMENT PLUGS		
PLUG	TOP (MD)	BOTTOM (MD)

32. FORMATION DETAILS and STRATIGRAPHIC MARKERS				
FR	FORMATION NAME	TOP (MD)	TOP (TVD)	DESCRIPTION, CONTENTS, ETC.
1	UTELAND BUTTE	6960	6960	Shale
	OIL SHOW? ☐ GAS SHOW? ☐ WATER FLOW? ☐ DRILL STEM TESTED? ☐ CORED? ☐ COMPLETED OR TESTED? ☒ COMMINGLED? ☐			

33. COMPLETED and TESTED INTERVALS (Formation Reference (FR) 1, 2, 3, ..., etc. as in Section 32.)						
FR	TOP (MD)	BOTTOM (MD)	TOP (TVD)	BOTTOM (TVD)	STIMULATION TREATMENT	INTERVAL STATUS
1	6960	17363			Fracture Stimulated	PRODUCING


34A. PRODUCTION INFORMATION (Formation Reference (FR) 1, 2, 3, ..., etc. as in Section 32.)									
FR	TOP (MD)	BOTTOM (MD)	DATE FIRST PROD.	TEST DATE	HRS. TESTED	TBG. PRESSURE	CSG. PRESSURE	PROD. METHOD	
1	6960	17363	08/01/2024	08/13/2024	6	905		Flowing	
	TEST PRODUCTION VOLUMES			24-HOUR PRODUCTION RATES			GAS-OIL RATIO	OIL API	GAS BTU
	OIL (BBL)	GAS (MSCF)	WATER (BBL)	OIL (BBL)	GAS (MSCF)	WATER (BBL)	465	38.7	0.8360
	217	101	567	868	404	2268			

35. WELL TREATMENTS (Formation Reference (FR) 1, 2, 3, ..., etc. as in Section 32.)						
FR	TREATMENT TYPE	TOP (MD)	BOTTOM (MD)	START DATE	END DATE	AMOUNT AND TYPE OF MATERIAL
1	Fracture Stimulation	6960	17363	06/10/2024	07/08/2024	593216 bbl slickwater 25869875 lbs local sand 43 stages

36. LOGS, SURVEYS, AND REPORTS (PDF file of each and LAS file of logs if available are to be submitted.)		
REPORTS AND OTHER INFORMATION.		
Dx Survey ☐	DST Report ☐	Core Analysis ☐
DOG M Form 7 ☐	Geologic Report ☐	Wellbore Diagram ☒
Other ☐		
SUBMITTED PDF LOGS		SUBMITTED LAS LOGS
CEMENT BOND		CEMENT BOND


OGM Official Use Only

37. I hereby certify that the foregoing and attached information is complete as determined from all available records.		
NAME	TITLE	DATE
Don Hamilton	Permitting Agent	10/01/2024
SIGNATURE	PHONE	EMAIL
N/A	4356503866	starpoint@etv.net

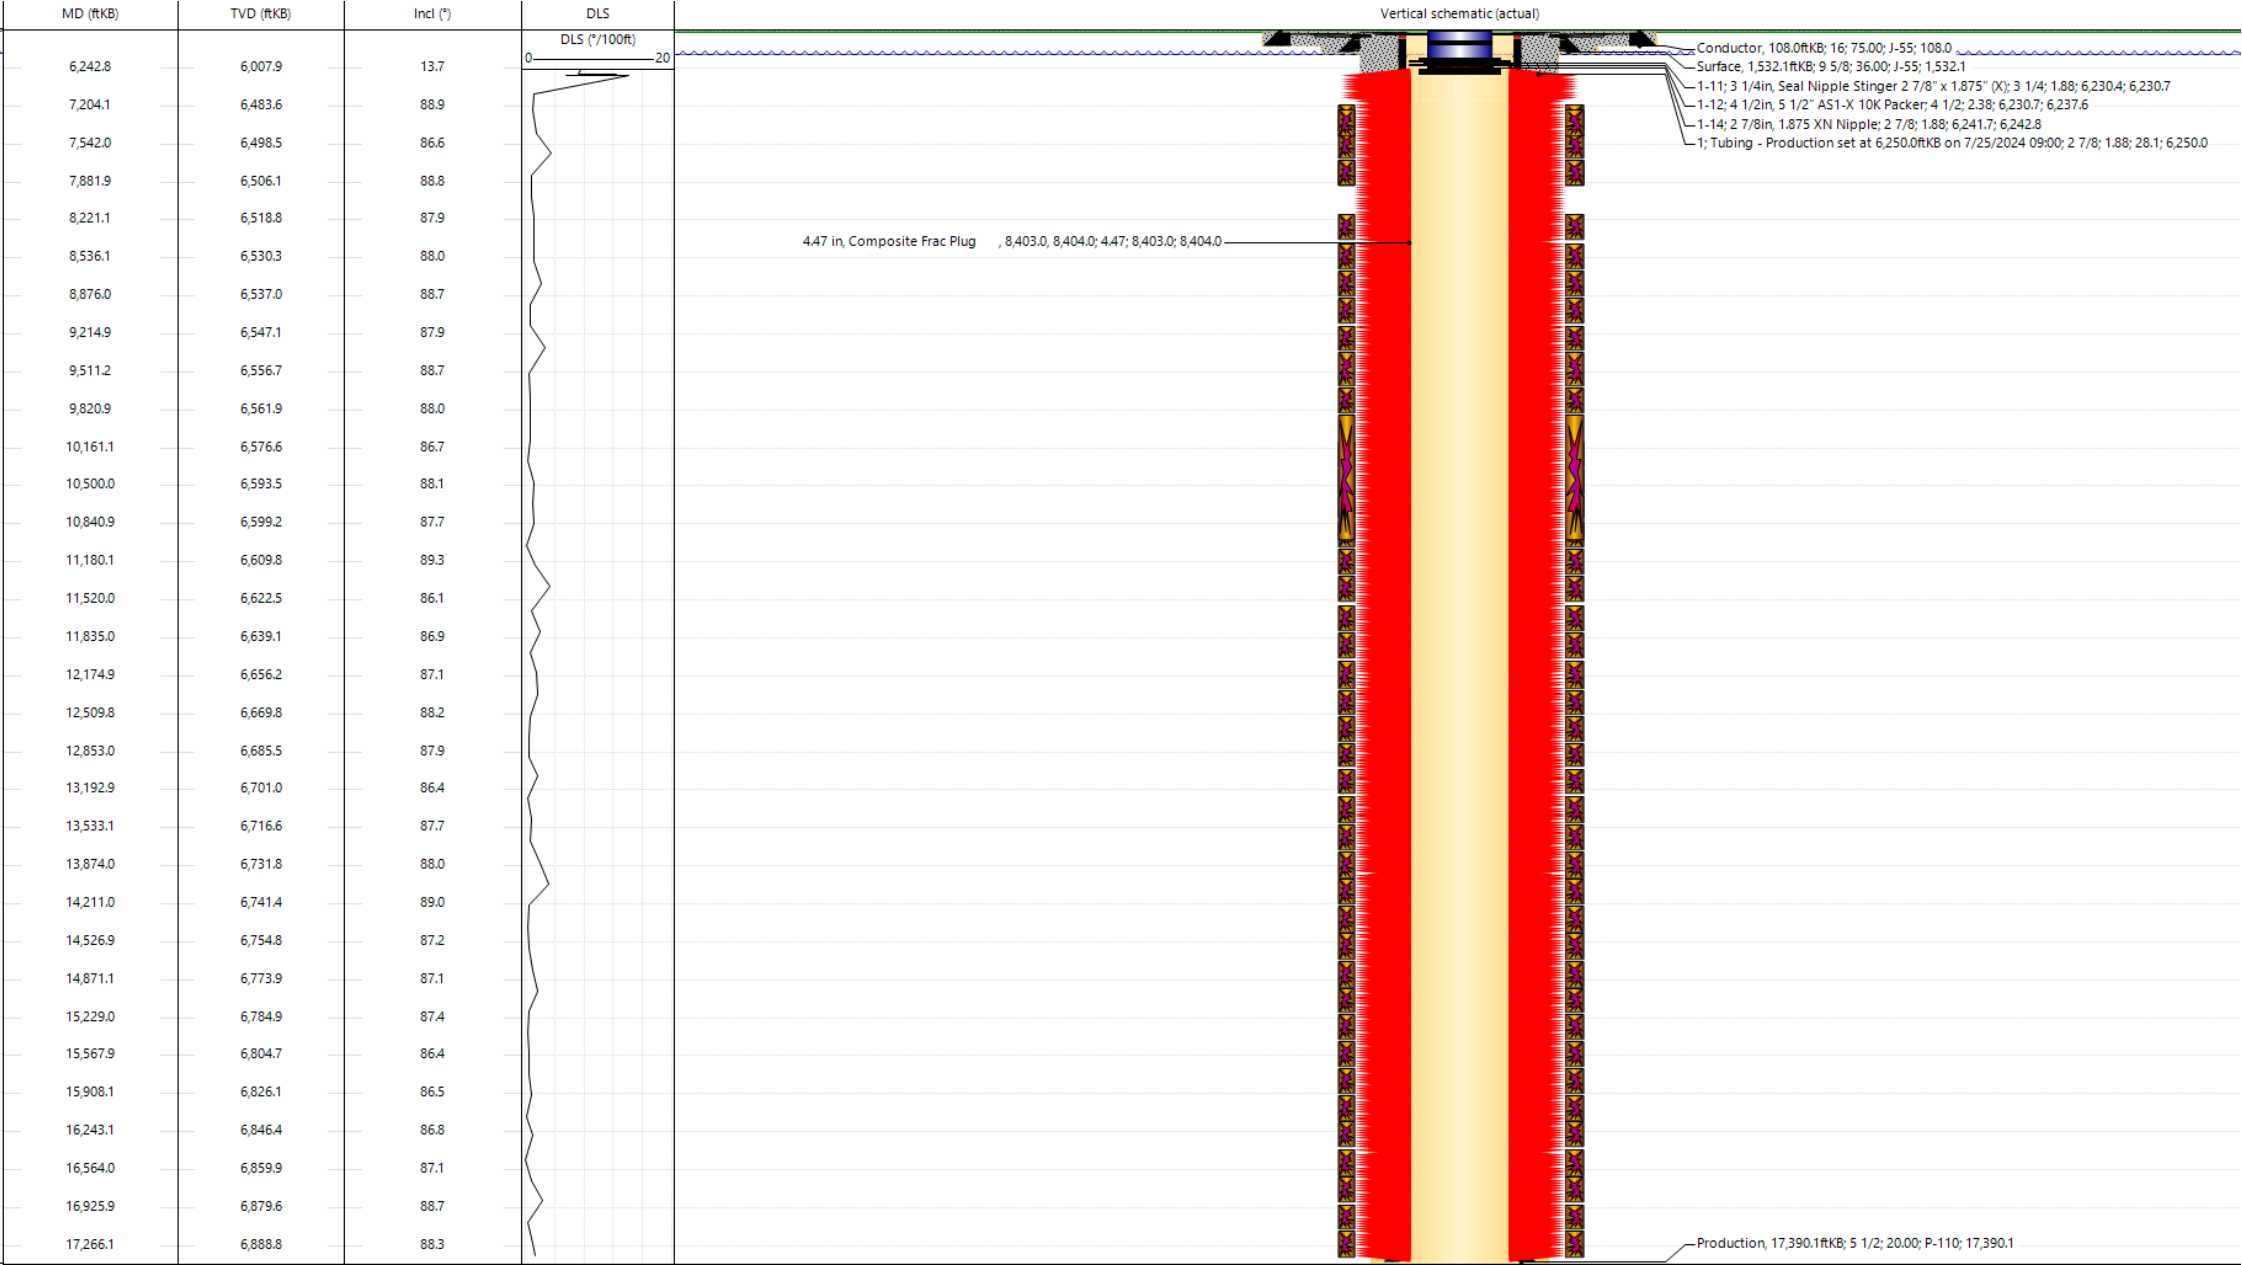


WELL LOCATION,
BRUTUS BUCKEYE 26-13-8-16-3H,
LOCATED AS SHOWN IN THE NW 1/4
SE 1/4 OF SECTION 26, T8S, R16E,
S.L.B.&M. DUCHESNE COUNTY, UTAH.

TARGET BOTTOM HOLE,
BRUTUS BUCKEYE 26-13-8-16-3H,
LOCATED AS SHOWN IN LOT 3 OF
SECTION 13, T8S, R16E, S.L.B.&M.
DUCHESNE COUNTY, UTAH.

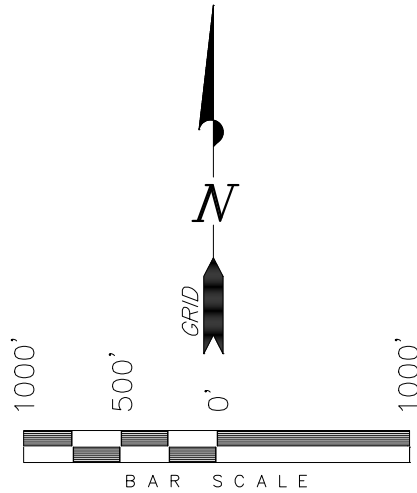

T8S, R16E, S.L.B.&M.

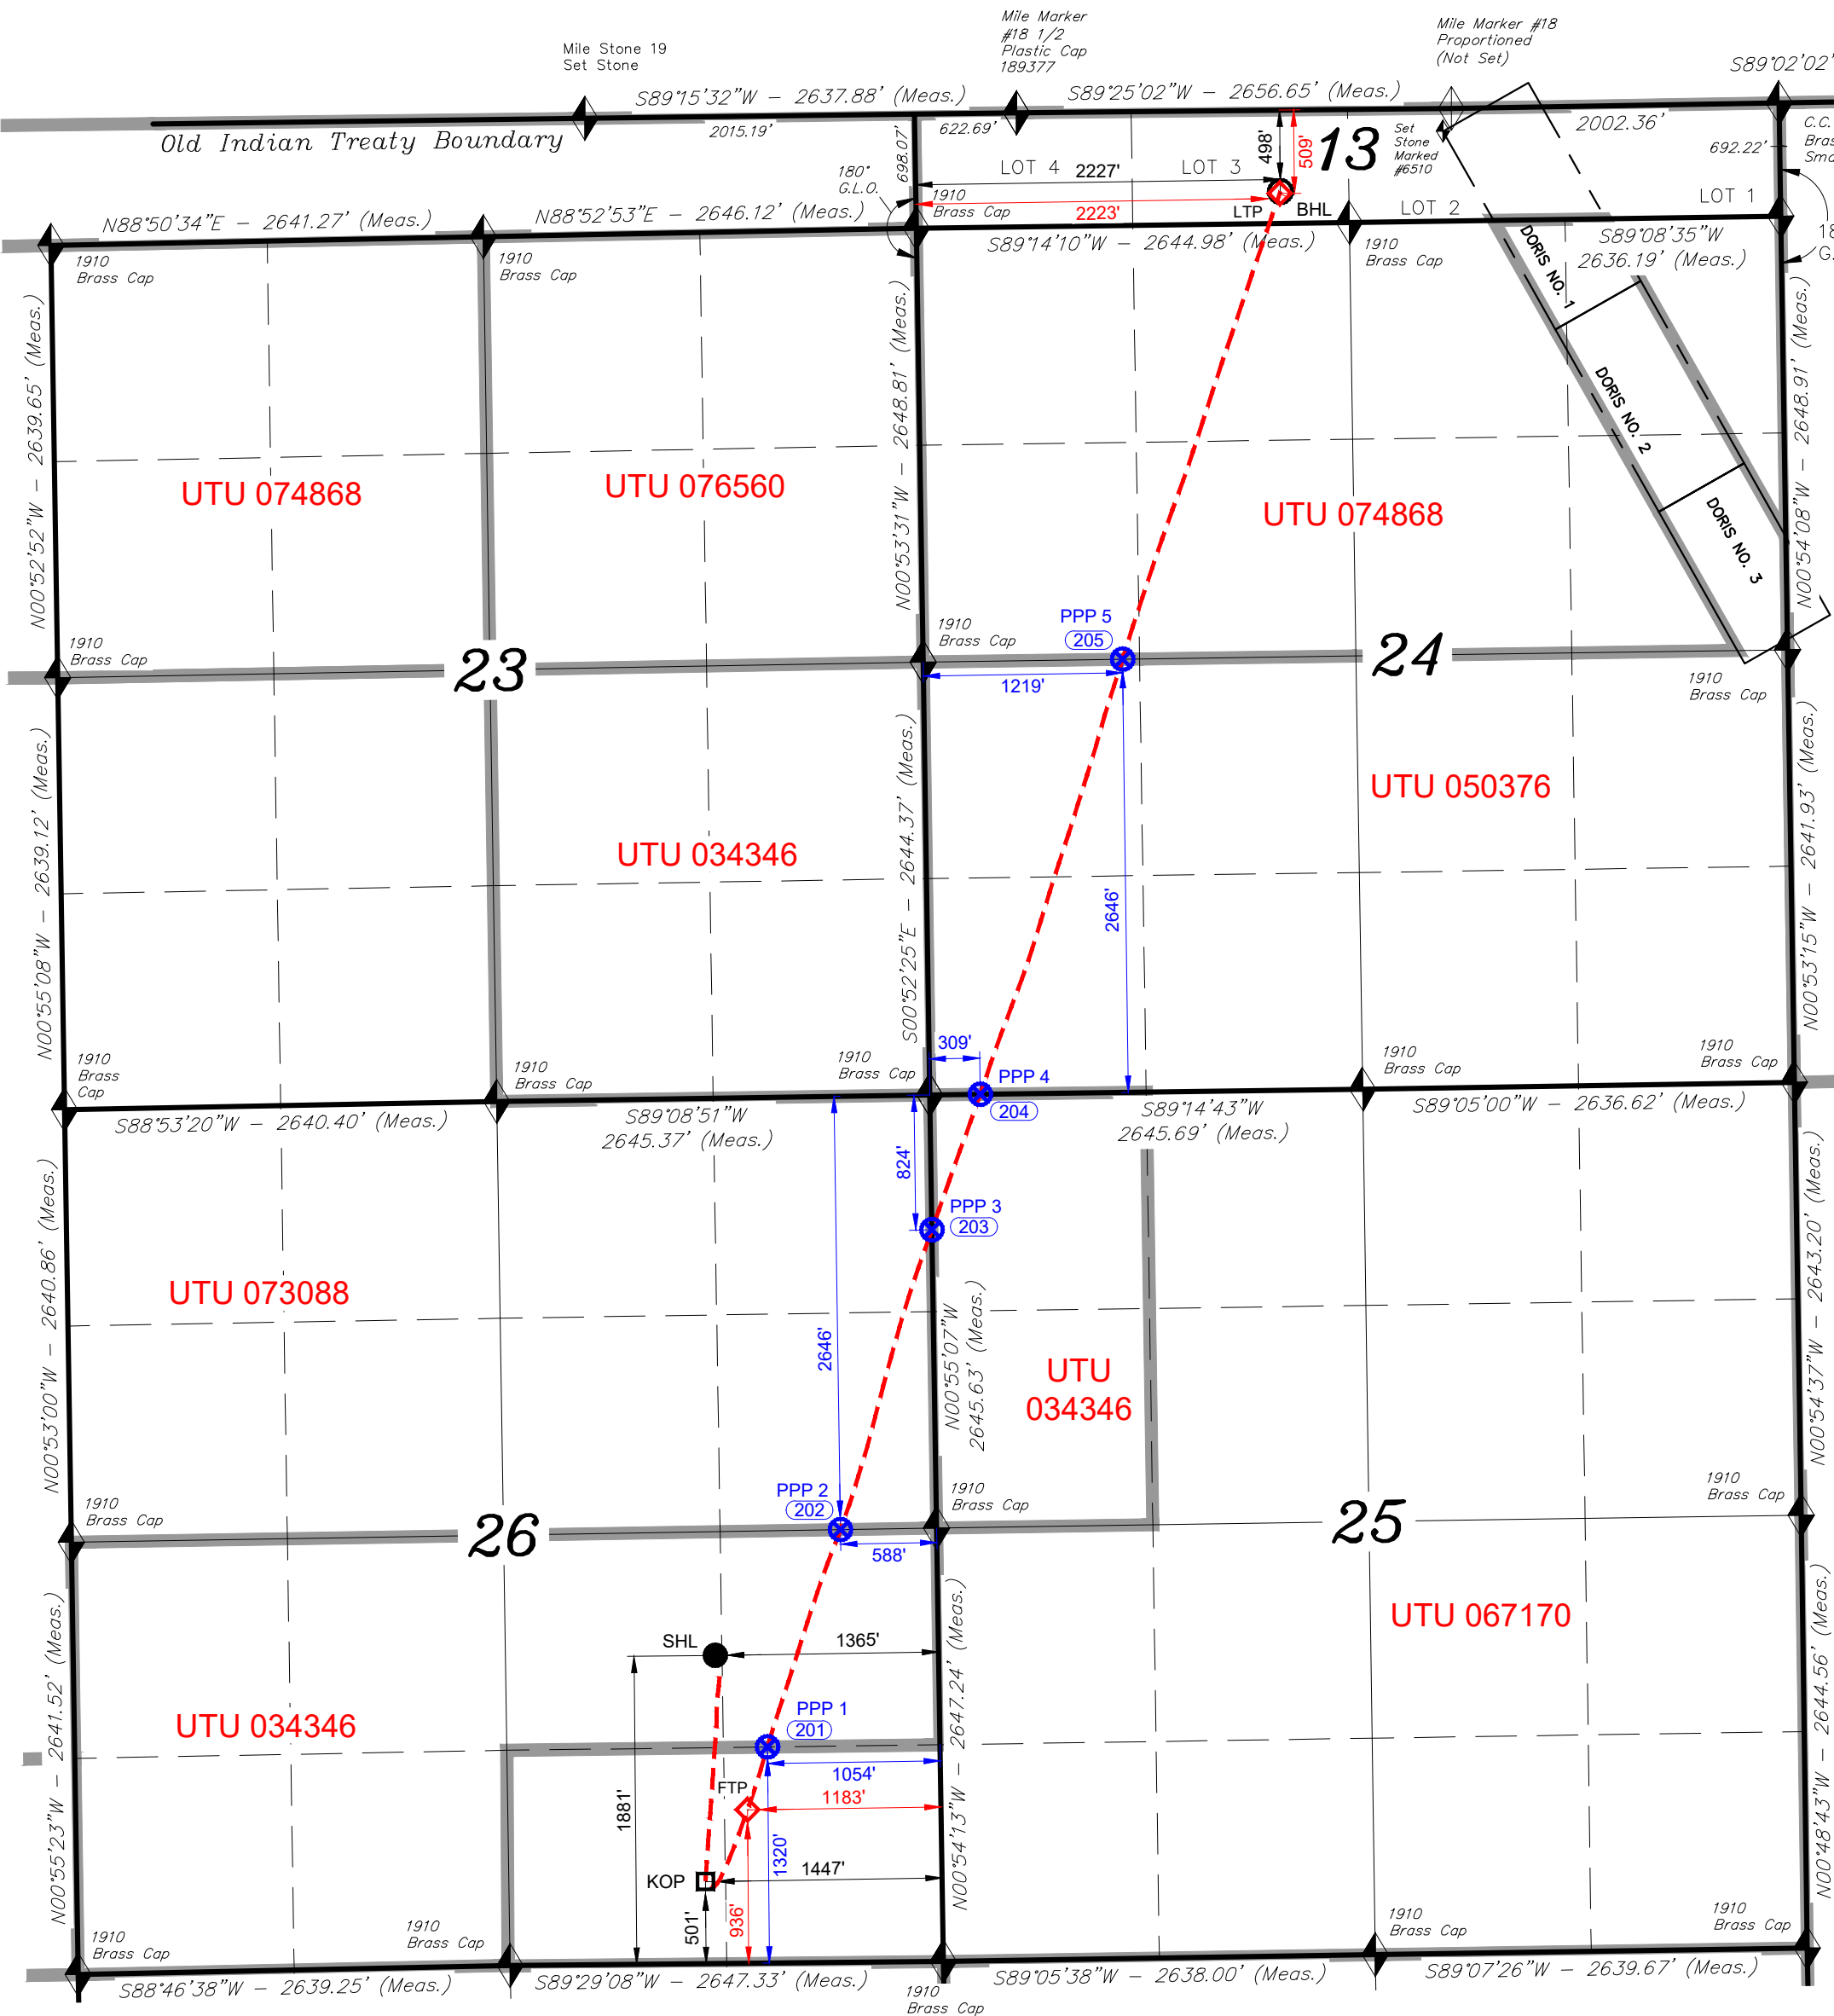

WELL LOCATION:
BRUTUS BUCKEYE 26-13-8-16-3H
ELEV. UNGRADED GROUND = 5512.9'

- NOTES:
- Well footages are measured at right angles to the Section Lines.
 - Bearings are based on Global Positioning Satellite Observations referencing Utah Central State Plane Grid North.

POINT TABLE				
POINT	LATITUDE	LONGITUDE	NORTHING (NAD 83)	EASTING (NAD 83)
201	N40° 05' 06.98"	W110° 04' 51.52"	7202934.2566	2037425.9029
202	N40° 05' 20.03"	W110° 04' 45.52"	7204260.9901	2037871.2732
203	N40° 05' 38.03"	W110° 04' 37.96"	7206091.4568	2038429.8059
204	N40° 05' 46.16"	W110° 04' 33.99"	7206918.9528	2038725.2075
205	N40° 06' 12.27"	W110° 04' 22.26"	7209575.2156	2039594.2908

SURFACE LOCATION	
NAD 83 (SURFACE LOCATION)	
LATITUDE =	40°05'12.56" (40.086821)
LONGITUDE =	110°04'55.52" (110.082088)
NAD 27 (SURFACE LOCATION)	
LATITUDE =	40°05'12.69" (40.086859)
LONGITUDE =	110°04'52.97" (110.081382)
UTM NAD 83 ZONE N12 METERS	
N =	4437797.240
E =	578253.948

BASIS OF ELEV: Elevations are based on an N.G.S. OPUS Correction. LOCATION: LAT. 40°04'09.56" LONG. 110°00'43.28" (Tristate Aluminum Cap) Elev. 5281.57'

KICK OFF POINT	
NAD 83 (KICK OFF POINT)	
LATITUDE =	40°04'58.92" (40.083033)
LONGITUDE =	110°04'56.57" (110.082380)
NAD 27 (KICK OFF POINT)	
LATITUDE =	40°04'59.06" (40.083071)
LONGITUDE =	110°04'54.03" (110.081674)
UTM NAD 83 ZONE N12 METERS	
N =	4437376.558
E =	578233.399

FIRST TAKE POINT	
NAD 83 (FIRST TAKE POINT)	
LATITUDE =	40°05'03.20" (40.084223)
LONGITUDE =	110°04'53.17" (110.081437)
NAD 27 (FIRST TAKE POINT)	
LATITUDE =	40°05'03.34" (40.084262)
LONGITUDE =	110°04'50.63" (110.080731)
UTM NAD 83 ZONE N12 METERS	
N =	4437509.505
E =	578312.382

LAST TAKE POINT	
NAD 83 (LAST TAKE POINT)	
LATITUDE =	40°06'40.22" (40.111172)
LONGITUDE =	110°04'09.33" (110.069258)
NAD 27 (LAST TAKE POINT)	
LATITUDE =	40°06'40.36" (40.111210)
LONGITUDE =	110°04'06.79" (110.068552)
UTM NAD 83 ZONE N12 METERS	
N =	4440511.388
E =	579319.481

BOTTOM OF HOLE	
NAD 83 (BOTTOM OF HOLE)	
LATITUDE =	40°06'40.33" (40.111203)
LONGITUDE =	110°04'09.28" (110.069243)
NAD 27 (BOTTOM OF HOLE)	
LATITUDE =	40°06'40.47" (40.111241)
LONGITUDE =	110°04'06.73" (110.068537)
UTM NAD 83 ZONE N12 METERS	
N =	4440514.839
E =	579320.685

SURVEYED BY: S.H.
DRAWN BY: F.T.M.
DATE: 08-23-23
SCALE: 1" = 1000'
REVISED:

- PROPOSED WELLHEAD
◻ KICK OFF POINT
◻ TAKE POINT
⊗ PPP
○ TARGET BOTTOM HOLE
- ◆ SECTION CORNERS LOCATED
◇ SECTION CORNERS COMPUTED

THIS IS TO CERTIFY THAT THE ABOVE SURVEY WAS PREPARED FROM FIELD NOTES AND SURVEYS MADE BY ME OR UNDER MY SUPERVISION AND THAT THE SAME ARE TRUE AND CORRECT TO THE BEST OF MY KNOWLEDGE AND BELIEF.

10003
REGISTERED LAND SURVEYOR
STATE OF UTAH
STACY W.

