

STATE OF UTAH
DEPARTMENT OF NATURAL RESOURCES
DIVISION OF OIL, GAS AND MINING

FORM 8

WELL COMPLETION OR RECOMPLETION REPORT AND LOG

1. WELL NAME
Brutus Buckeye 26-13-8-16-4H

2. TYPE OF WELL
Oil Well

3. TYPE OF WORK
DRILL NEW ☒ REENTER P&A ☐ DEEPEN ☐ RECOMP ☐

4. API NUMBER
4301354613

5. NAME OF OPERATOR
Scout Energy Management, LLC

6. OPERATOR PHONE
972-325-1027

7. FIELD NAME
MONUMENT BUTTE

8. ADDRESS OF OPERATOR
13800 Montfort Drive, Suite 100, Dallas, TX, 75240

9. OPERATOR E-MAIL
tbrown@scoutep.com

10. UNIT NAME
Greater Monument Butte

11. MINERAL LEASE NUMBER
MULTIPLE LEASES

12. MINERAL OWNERSHIP
FEDERAL

13. SURFACE OWNERSHIP
FEDERAL

14. COUNTY
DUCHESNE

15. DATE SPUDDED (SPUD RIG)
01/05/2024

16. DATE SPUDDED (ROTARY RIG)
02/25/2024

17. DATE TOTAL DEPTH REACHED
03/08/2024

18. DATE COMPLETED/ABANDONED
07/26/2024

19. DATE OF FIRST PROD. / INJ.
PROD:10/01/2024 INJ:

20. DEPTH REFERENCE
GROUND LEVEL ☒ KELLY BUSHING ☐ DERRICK FLOOR ☐

21. DEPTH REFERENCE ELEVATION
5571 (US Feet)

22. GRADED GROUND LEVEL ELEVATION
5571 (US Feet)

23. WELLBORE DEVIATION PROFILE
VERTICAL ☐ DIRECTIONAL ☐ HORIZONTAL ☒

24. TOTAL DEPTH
MD 17482 TVD 6874

25. PLUGGED BACK TOTAL DEPTH
MD TVD

26. CURRENT WELL STATUS
Producing

27. LOCATION OF WELL									
WELL POSITION	FOOTAGES		QTR-QTR	SECTION	TOWNSHIP	RANGE	MERIDIAN	UTM EASTING	UTM NORTHING
Surface	1882 FSL	1385 FEL	NWSE	26	8.0 S	16.0 E	S	578248	4437797
Producing Interval Top	1080 FSL	2436 FEL	SWSE	26	8.0 S	16.0 E	S		
Producing Interval Bottom	608 FNL	759 FWL	LOT4	13	8.0 S	16.0 E	S		
Total Depth	516 FNL	788 FWL	LOT4	13	8.0 S	16.0 E	S		

28. HOLE, CASING AND CEMENT INFORMATION															
STRING	HOLE SIZE	CASING O.D.	WEIGHT	GRADE	THREAD	TOP (MD)	BOTTOM (MD)	DV TOOL DEPTH	LEAD TAIL	CEMENT TYPE	SACKS	YIELD	WEIGHT	CEMENT TOP	BASIS FOR TOP
COND	24.0	16.0	65.0			0	108		TO	Class G Cement	100	1.17	15.8	0	Circulate
SURF	12.25	9.625	36.0	J-55	BTC	0	1531		L	Class G Cement	330	1.77	13.1	0	Circulate
									T	Class G Cement	250	1.16	15.8		
PROD	8.75	5.5	20.0	P-110	BTC	0	6319		L	Class G Cement	600	2.92	11.5	0	Circulate
P2	7.875	5.5	20.0	P-110	BTC	6319	17382		T	Class G Cement	2000	1.43	14.0		

29. TUBING RECORD			
TUBING SIZE	TOP (MD)	BOT (MD)	PACKER DEPTH
2.725	0	6000	5961

30. RETRIEVABLE / TEMPORARY PLUGS		
PLUG	DEPTH (MD)	TYPE

31. PERMANENT / ABANDONMENT PLUGS		
PLUG	TOP (MD)	BOTTOM (MD)

32. FORMATION DETAILS and STRATIGRAPHIC MARKERS				
FR	FORMATION NAME	TOP (MD)	TOP (TVD)	DESCRIPTION, CONTENTS, ETC.
1	UTELAND BUTTE	7250	7250	Shale
	OIL SHOW? ☐ GAS SHOW? ☐ WATER FLOW? ☐ DRILL STEM TESTED? ☐ CORED? ☐ COMPLETED OR TESTED? ☒ COMMINGLED? ☐			

33. COMPLETED and TESTED INTERVALS (Formation Reference (FR) 1, 2, 3, ..., etc. as in Section 32.)						
FR	TOP (MD)	BOTTOM (MD)	TOP (TVD)	BOTTOM (TVD)	STIMULATION TREATMENT	INTERVAL STATUS
1	7250	17354			Fracture Stimulated	PRODUCING


34A. PRODUCTION INFORMATION (Formation Reference (FR) 1, 2, 3, ..., etc. as in Section 32.)									
FR	TOP (MD)	BOTTOM (MD)	DATE FIRST PROD.	TEST DATE	HRS. TESTED	TBG. PRESSURE	CSG. PRESSURE	PROD. METHOD	
1	7250	17354	10/01/2024	10/13/2024	6	902	0	Flowing	
	TEST PRODUCTION VOLUMES			24-HOUR PRODUCTION RATES			GAS-OIL RATIO	OIL API	GAS BTU
	OIL (BBL)	GAS (MSCF)	WATER (BBL)	OIL (BBL)	GAS (MSCF)	WATER (BBL)	558	38.7	0.8360
	172	96	649	688	384	2596			

35. WELL TREATMENTS (Formation Reference (FR) 1, 2, 3, ..., etc. as in Section 32.)						
FR	TREATMENT TYPE	TOP (MD)	BOTTOM (MD)	START DATE	END DATE	AMOUNT AND TYPE OF MATERIAL
1		7250	17354	06/10/2024	07/08/2024	579420 bbl slickwater 24268250 lbs local sand 42 stages

36. LOGS, SURVEYS, AND REPORTS (PDF file of each and LAS file of logs if available are to be submitted.)		
REPORTS AND OTHER INFORMATION.		
Dx Survey ☐	DST Report ☐	Core Analysis ☐
DOG M Form 7 ☐	Geologic Report ☐	Wellbore Diagram ☒
Other ☒		
SUBMITTED PDF LOGS		SUBMITTED LAS LOGS
CEMENT BOND		CEMENT BOND


OGM Official Use Only

37. I hereby certify that the foregoing and attached information is complete as determined from all available records.		
NAME	TITLE	DATE
Don Hamilton	Permitting Agent	10/01/2024
SIGNATURE	PHONE	EMAIL
N/A	4356503866	starpoint@etv.net

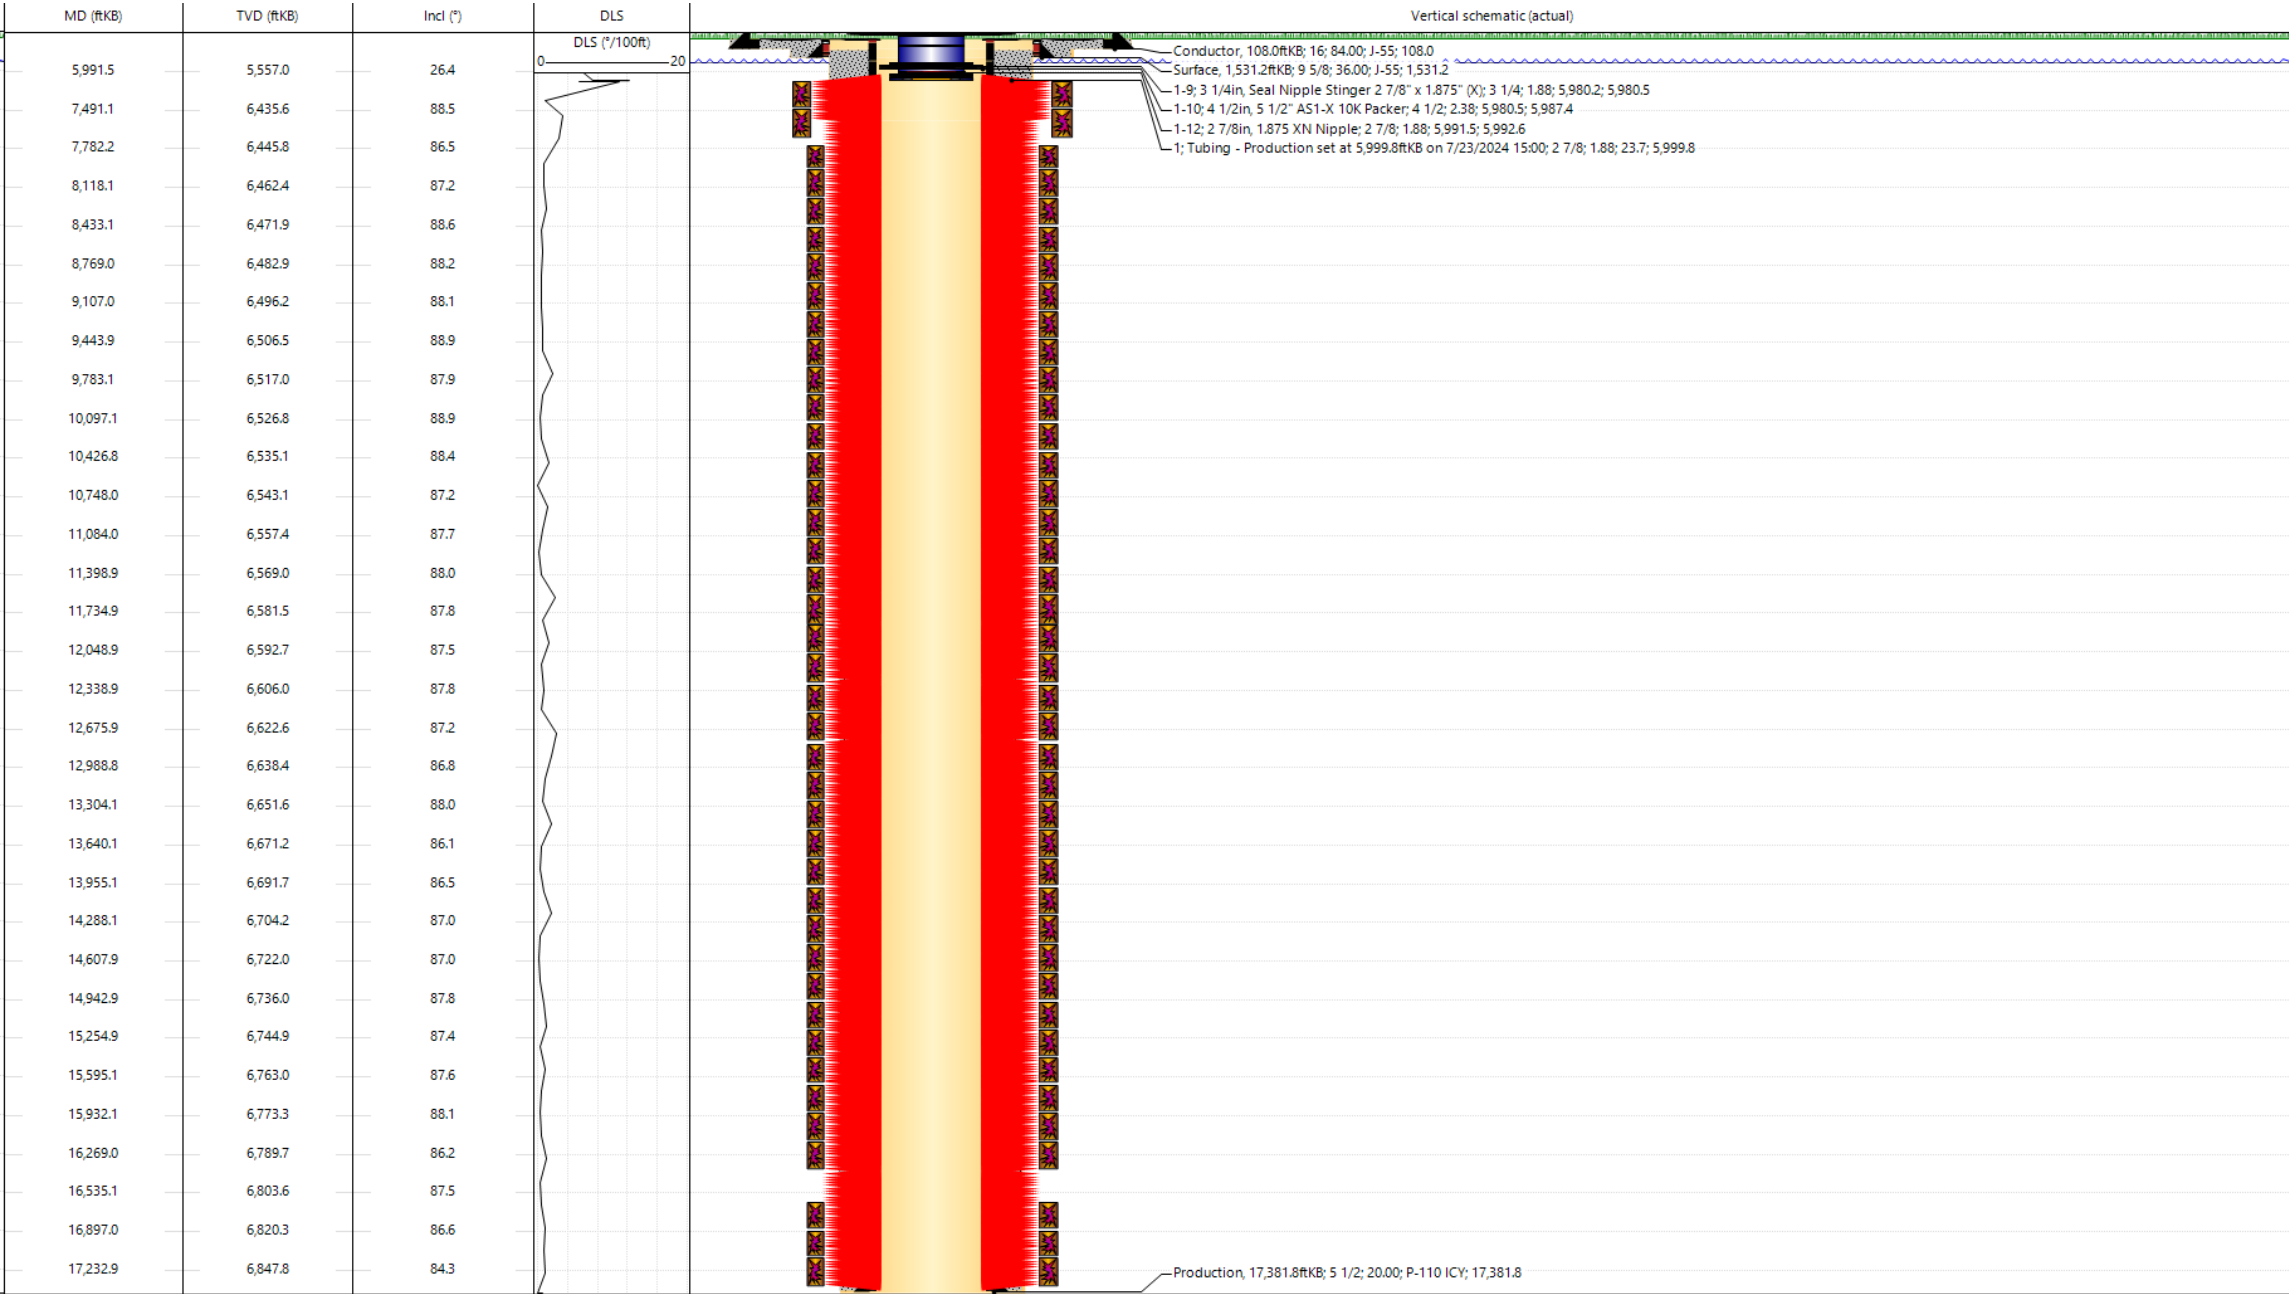


WELL LOCATION,
BRUTUS BUCKEYE 26-13-8-16-4H,
LOCATED AS SHOWN IN THE NW 1/4
SE 1/4 OF SECTION 26, T8S, R16E,
S.L.B.&M. DUCHESNE COUNTY, UTAH.

TARGET BOTTOM HOLE,
BRUTUS BUCKEYE 26-13-8-16-4H,
LOCATED AS SHOWN IN LOT 4
(SW 1/4 SW 1/4) OF SECTION 13,
T8S, R16E, S.L.B.&M. DUCHESNE
COUNTY, UTAH.

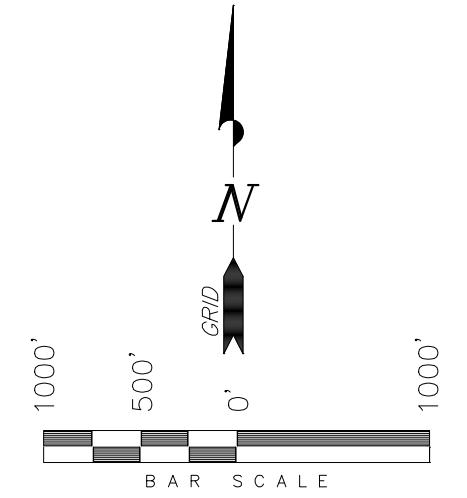

T8S, R16E, S.L.B.&M.

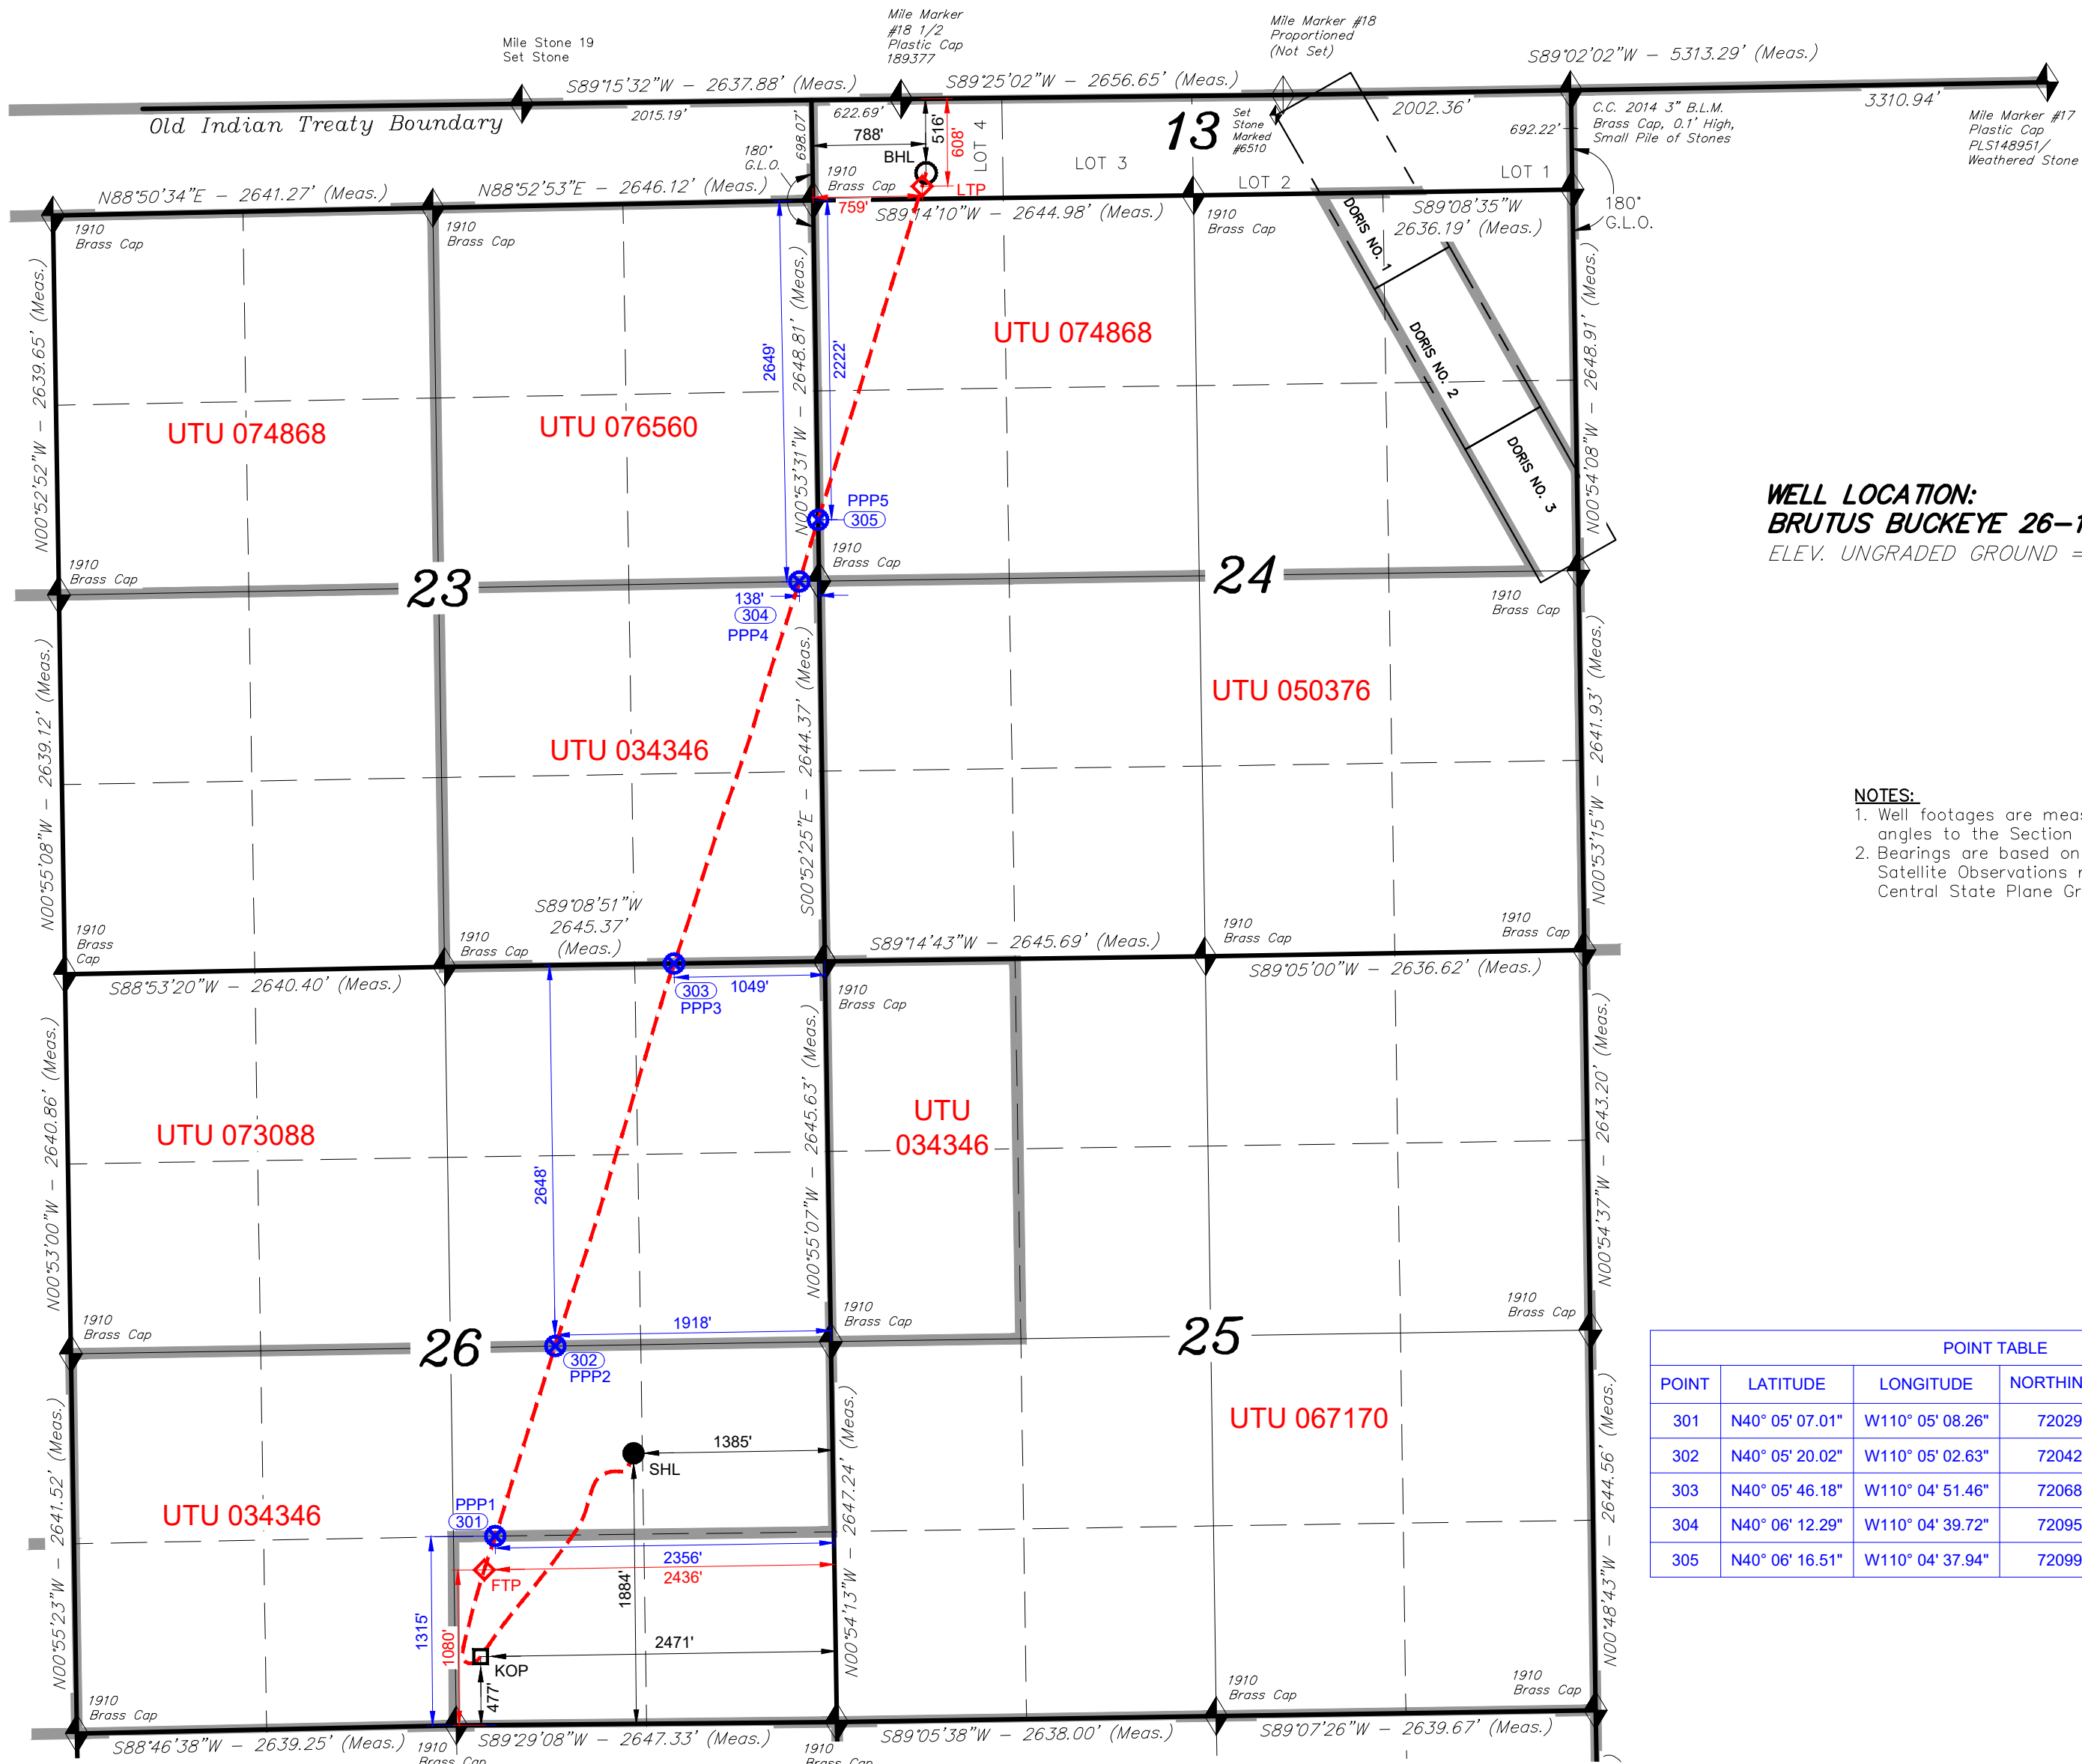

WELL LOCATION:
BRUTUS BUCKEYE 26-13-8-16-4H
ELEV. UNGRADED GROUND = 5514.0'

- NOTES:
- Well footages are measured at right angles to the Section Lines.
 - Bearings are based on Global Positioning Satellite Observations referencing Utah Central State Plane Grid North.

POINT TABLE				
POINT	LATITUDE	LONGITUDE	NORTHING (NAD 83)	EASTING (NAD 83)
301	N40° 05' 07.01"	W110° 05' 08.26"	7202915.8835	2036125.3379
302	N40° 05' 20.02"	W110° 05' 02.63"	7204239.4143	2036542.0624
303	N40° 05' 46.18"	W110° 04' 51.46"	7206899.2828	2037367.8012
304	N40° 06' 12.29"	W110° 04' 39.72"	7209555.5144	2038238.4322
305	N40° 06' 16.51"	W110° 04' 37.94"	7209985.0846	2038369.6509

SURFACE LOCATION	
NAD 83 (SURFACE LOCATION)	
LATITUDE =	40°05'12.56" (40.086822)
LONGITUDE =	110°04'55.78" (110.082160)
NAD 27 (SURFACE LOCATION)	
LATITUDE =	40°05'12.70" (40.086860)
LONGITUDE =	110°04'53.23" (110.081454)
UTM NAD 83 ZONE N12 METERS	
N =	4437797.286
E =	578247.807

BASIS OF ELEV: Elevations are based on an N.G.S. OPUS Correction. LOCATION: LAT. 40°04'09.56" LONG. 110°00'43.28" (Tristate Aluminum Cap) Elev. 5281.57'

KICK OFF POINT	
NAD 83 (KICK OFF POINT)	
LATITUDE =	40°04'58.75" (40.082987)
LONGITUDE =	110°05'09.75" (110.086041)
NAD 27 (KICK OFF POINT)	
LATITUDE =	40°04'58.89" (40.083025)
LONGITUDE =	110°05'07.21" (110.085335)
UTM NAD 83 ZONE N12 METERS	
N =	4437368.172
E =	577921.301

FIRST TAKE POINT	
NAD 83 (FIRST TAKE POINT)	
LATITUDE =	40°05'04.71" (40.084642)
LONGITUDE =	110°05'09.29" (110.085915)
NAD 27 (FIRST TAKE POINT)	
LATITUDE =	40°05'04.85" (40.084680)
LONGITUDE =	110°05'06.75" (110.085209)
UTM NAD 83 ZONE N12 METERS	
N =	4437552.033
E =	577930.145

LAST TAKE POINT	
NAD 83 (LAST TAKE POINT)	
LATITUDE =	40°06'39.32" (40.110922)
LONGITUDE =	110°04'28.16" (110.074489)
NAD 27 (LAST TAKE POINT)	
LATITUDE =	40°06'39.46" (40.110961)
LONGITUDE =	110°04'25.62" (110.073783)
UTM NAD 83 ZONE N12 METERS	
N =	4440479.042
E =	578873.920

BOTTOM OF HOLE	
NAD 83 (BOTTOM OF HOLE)	
LATITUDE =	40°06'40.23" (40.111174)
LONGITUDE =	110°04'27.79" (110.074386)
NAD 27 (BOTTOM OF HOLE)	
LATITUDE =	40°06'40.37" (40.111213)
LONGITUDE =	110°04'25.25" (110.073680)
UTM NAD 83 ZONE N12 METERS	
N =	4440507.133
E =	578882.471

SURVEYED BY: S.H.
DRAWN BY: F.T.M.
DATE: 08-23-23
SCALE: 1" = 1000'
REVISED:



THIS IS TO CERTIFY THAT THE ABOVE SURVEY WAS PREPARED FROM FIELD NOTES AND PLANS MADE BY ME OR UNDER MY SUPERVISION AND THAT THE SAME ARE TRUE AND CORRECT TO THE BEST OF MY KNOWLEDGE AND BELIEF.

10003
R. B. 189377
08-28-2024
STACY W.
REGISTERED LAND SURVEYOR
STATE OF UTAH